
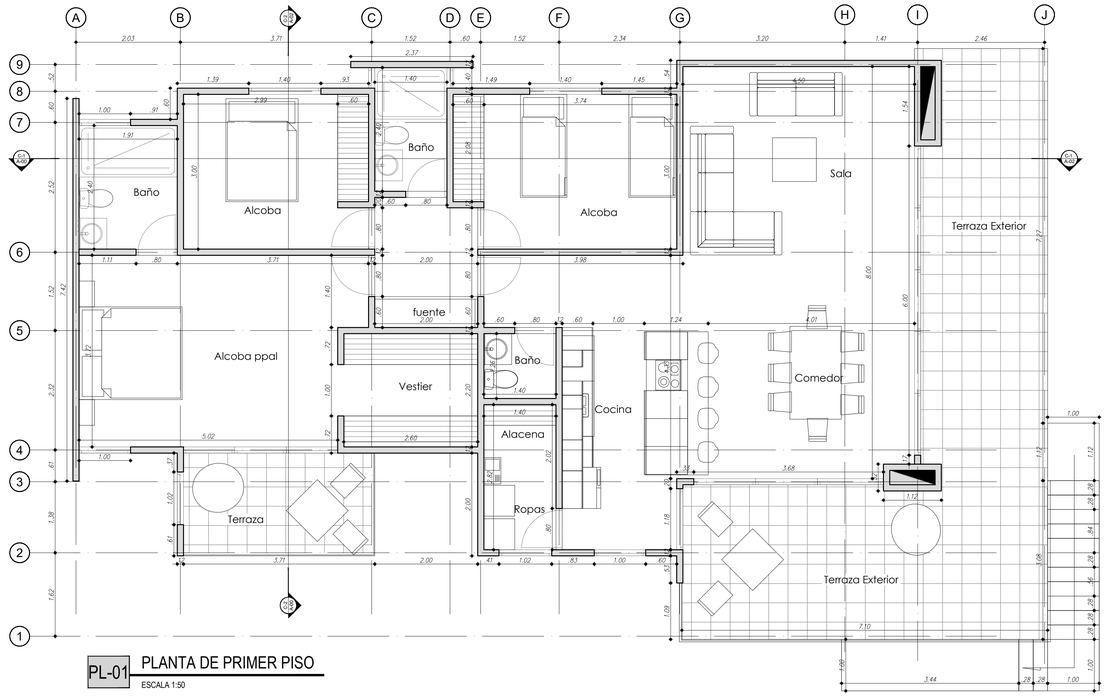



PL-01 PLANTA DE PRIMER PISO

ESCALA 1:50

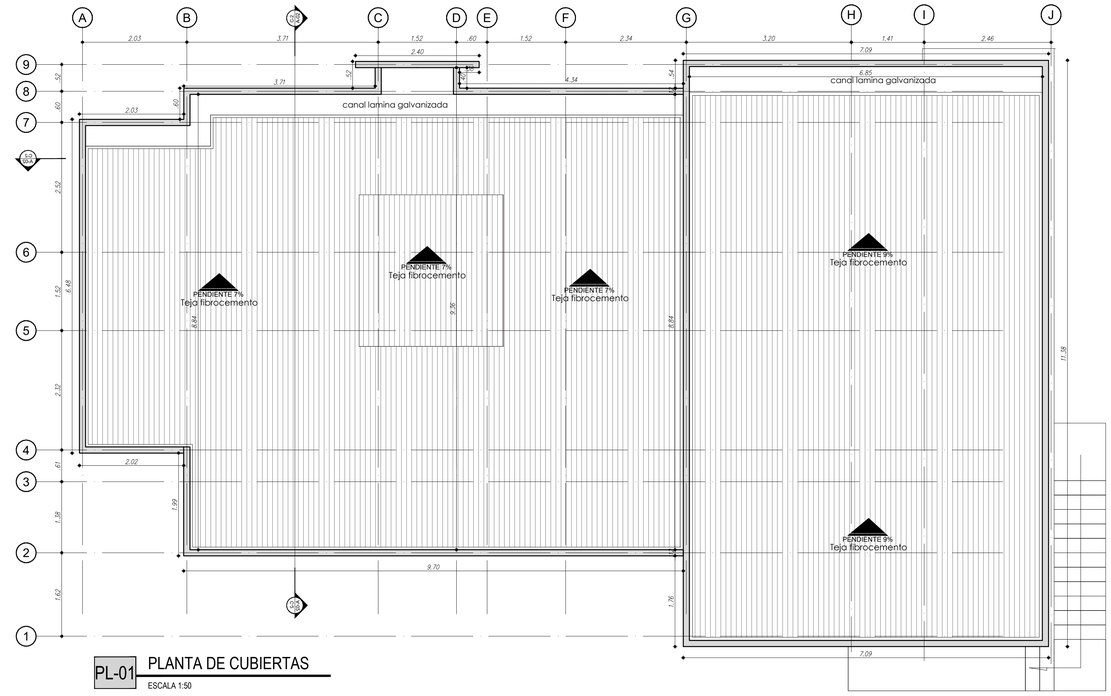


PL-01 PLANTA DE CUBIERTAS

ESCALA 1:50

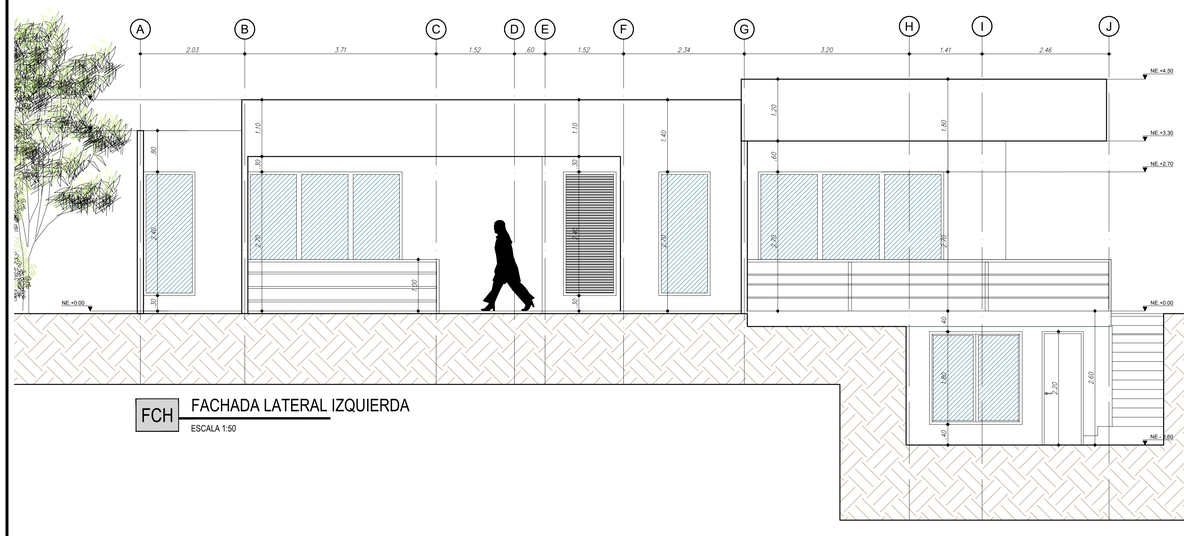

FCH FACHADA LATERAL IZQUIERDA

ESCALA 1:50

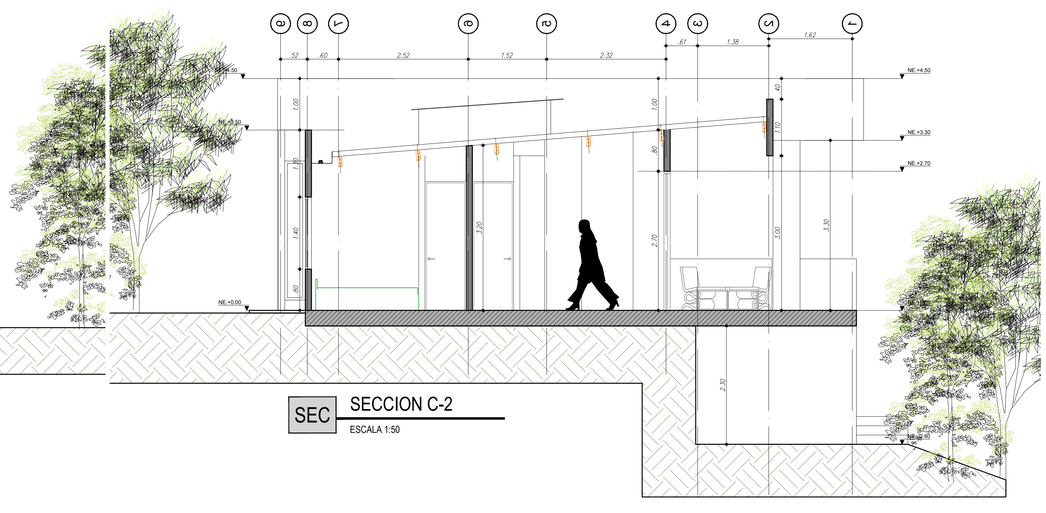

SEC SECCION C-2

ESCALA 1:50


K.3.18 — REQUISITOS ESPECÍFICOS PARA EDIFICACIONES PERTENECIENTES AL GRUPO DE OCUPACIÓN RESIDENCIAL (R)

K.3.18.1 — REQUISITOS ESPECÍFICOS PARA EDIFICACIONES DEL GRUPO DE OCUPACIÓN (R-1) — Los medios de evacuación de las edificaciones del Subgrupo de Ocupación Residencial Unifamiliar y Bifamiliar (R-1) deben cumplir los requisitos siguientes:

K.3.18.1.1 — *Número de salidas* — Se permite que haya una sola salida por piso en el caso de edificaciones unifamiliares y bifamiliares de las siguientes características: construida con materiales incombustibles, con una altura inferior a 9 m, un área por piso que no exceda de 200 m² y una distancia máxima de travesía de 15 m.

K.3.18.1.2 — *Medios de salida* — No es necesario que las puertas se abran en la misma dirección de evacuación.

(a) Las puertas de entrada y salida deben estar provistas de cerraduras y tener un sistema de iluminación adecuado.
(b) Se requiere que las puertas de las unidades de vivienda tengan cerraduras provistas de perillas con botón que impida la apertura por otro medio que facilite las llaves; puede, además, proveérseles de una cadena que facilite su apertura parcial y de un sistema de visión que permita a quien esté en el interior de la habitación, ver a cualquier persona colocada en la parte de afuera.
(c) Las ventanas dispuestas para su apertura deben estar dotadas de un sistema de cerradura en los marcos que sólo se abra desde el interior.

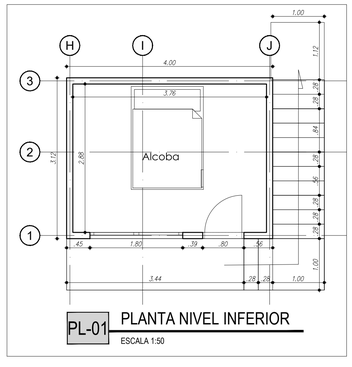

PL-01 PLANTA NIVEL INFERIOR

ESCALA 1:50

CUADRO DE AREAS

AREA LOTE		1500.00 M2
AREA PRIMER PISO		130.05 M2
AREA NIVEL INFERIOR		12.50 M2
Area Terrazas cubiertas		49.65 M2
Indice de ocupacion		56.88 %
Indice de construccion		5.88 %
TOTAL AREA CONSTRUIDA		192.20M2

VIVIENDA CAMPESTRE

PROYECTO:

Vereda La Cabaña, entrada a Rumichaca, Finca El Paraíso, Lote C - Manizales

PROPIETARIO

Regina Rivera Giraldo

CC 30319614

DISEÑO ARQUITECTONICO:

ARQUITECTO
FABIAN CIFUENTES
MP

ELEMENTOS NO ESTRUCTURALES:

OBSERVACIONES:

IMPRESION: MONOCHROME.CTB
COLOR: BLACK
LINEWEIGHT-USE OBJECT LINEWEIGHT

Se da cumplimiento a la resolución 5004 del 2018 y a sus modificaciones con respecto a los directrices trazadas por el RITEL

MODIFICACIONES

No.	OBSERVACION	FECHA
1		
2		
3		
4		
5		

CONTIENE:

ARQUITECTONICO

PLANTAS DE PRIMER PISO
NIVEL INFERIOR
PLANTA CUBIERTAS
CUADRO AREAS
FACHADA LATERAL IZQUIERDA
SECCION C-2

APROBO:

DIBUJO:

Digitec

Nestor Javier Sanchez Arcila
Celular: 3113333400
Email: nestorapin3@gmail.com

FECHA:

AGOSTO DE 2025

ESCALA:

1 : 50

PLANO:

1

DE:

2

ARQUITECTONICOS