

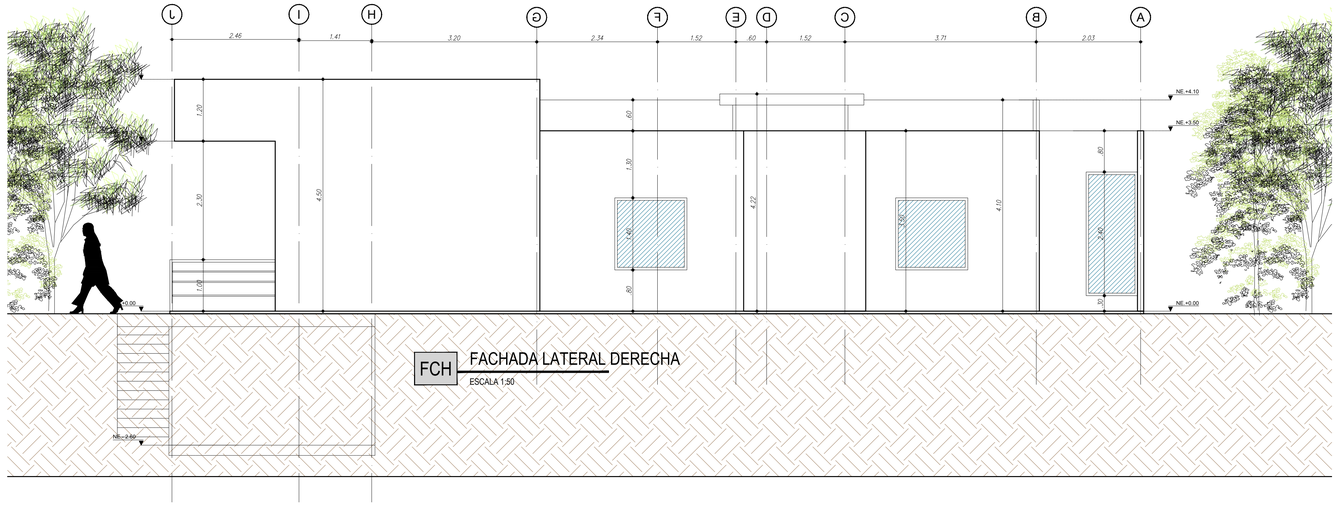



FCH FACHADA LATERAL DERECHA
ESCALA 1:50

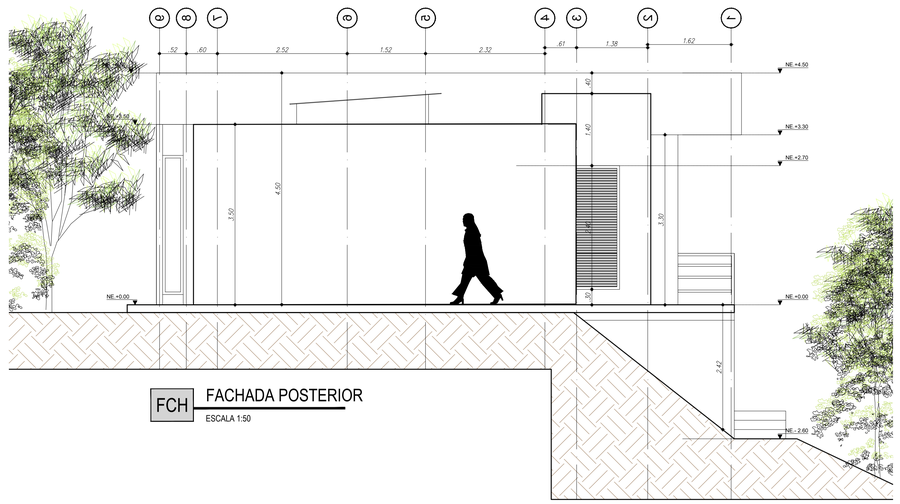

FCH FACHADA POSTERIOR
ESCALA 1:50

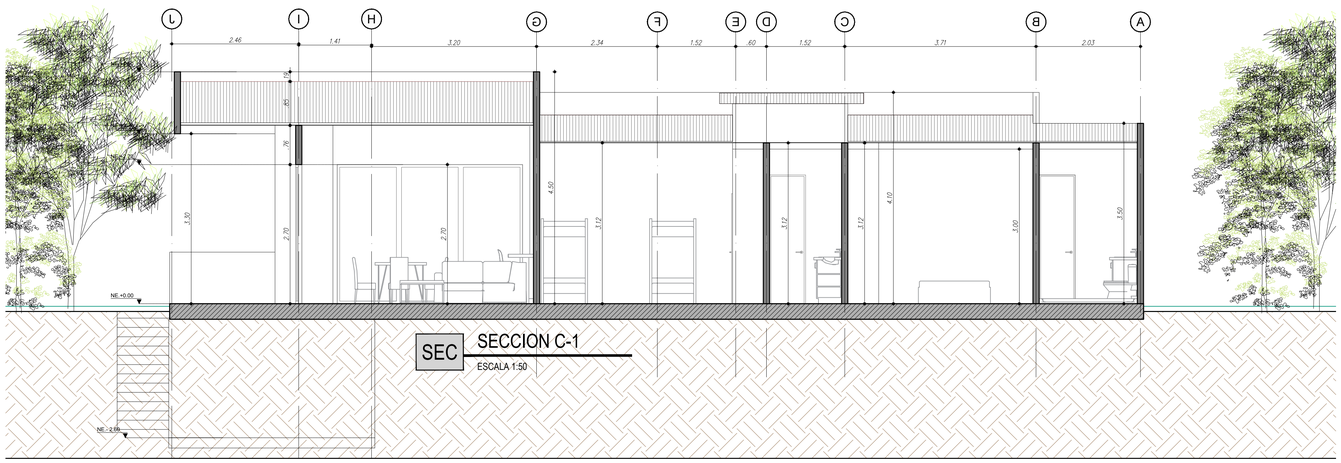

SEC SECCION C-1
ESCALA 1:50

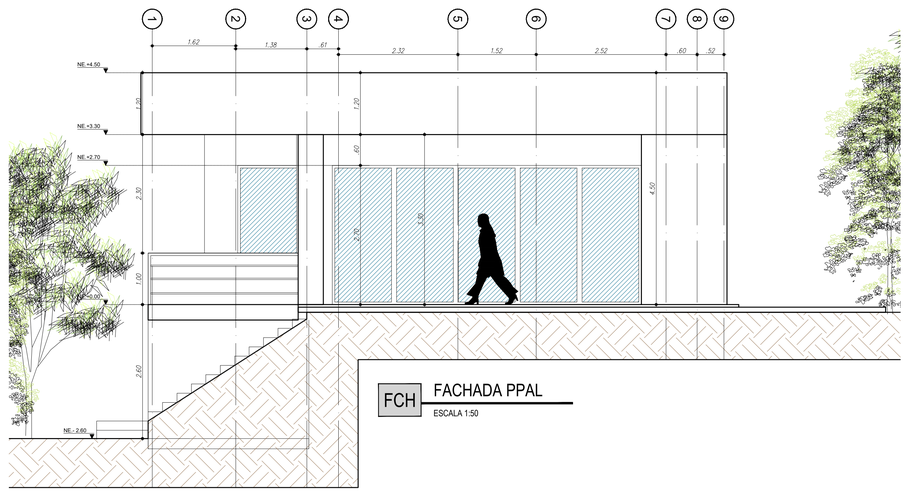

FCH FACHADA PPAL
ESCALA 1:50

Tabla K.3.3-1
Índice de Ocupación

M	Mixto y Otros	La mayoría área exigida para las ocupaciones que conforman la ocupación mixta de la edificación
P	Alta Peligrosidad	9
R	Residencial	18
T	Temporal y Misc.	Según ocupación

Tabla A.9.2-1
Grado de desempeño mínimo requerido

Grupo de Uso	Grado de desempeño
IV	Superior
III	Superior
II	Bueno
I	Bajo

Tabla A.9.5-1
Coeficiente de amplificación dinámica, ap, y tipo de anclajes o amarres requeridos, usado para determinar coeficiente de capacidad de disipación de energía, Rp, para elementos arquitectónicos y acabados

Elemento no estructural	a_p	Tipo de anclajes o amarre para determinar el coeficiente de capacidad de disipación de energía, Rp, mínimo requerido en A.9.4.9			
		Grado de desempeño			
		Superior	Bueno	Bajo	Materiales
Fachadas: Mampostería reforzada, separadas lateralmente de la estructura, apoyadas arriba y abajo.	1.0	Dúctiles	No Dúctiles	No Dúctiles	Ladrillo Farol
Muros Divisorios y Particiones: Muros divisorios de altura total.	1.0	No Dúctiles	No Dúctiles	Húmedos	Mamposteria
Cielo Rasos.	1.0	No Dúctiles	No Dúctiles	No Requerrido	GYPLAC
Tejas	1.0	No Dúctiles	No Dúctiles	No Requerrido	Fibrocemento

MEMORIAS J Y K VIVIENDA	
Grupo de Uso	Residencial
Subgrupo de uso *	R1 Unifamiliar -Bifamiliar
Carga de Ocupacion *	12
Numero de salidas *	
Distancia de recorrido hasta una salida *	PISO 1: 24.42 ML - PISO 2: 24,20ML
Capacidad de las Salidas *	Puertas: 0,80 m Escaleras: 0,90 m
Sistema y Equipo para detección y Alarma de Incendios	La vivienda estará protegidas mediante un sistema de alarma y detección de incendio, conformado por detectores con base sonora. J.4.2.8.1 Como la vivienda tiene más de 100 m2 de área construida, en caso de tener más de un detector el sistema debe estar interconectado de forma tal que la activación de un detector active a los demás. Para su diseño se tomará como referencia la norma NFPA 72.
Redes Electricas, de Gas y Otros Fluidos Combustibles	Para la protección de las instalaciones eléctricas internas de la vivienda se cumplirá con los requisitos dados en el Reglamento Técnico de Instalaciones Eléctricas, RETIE, y en el Código Eléctrico Colombiano.
La responsabilidad del cumplimiento del Título J - Requisitos de protección contra el fuego en edificaciones y el Título K – Otros requisitos complementarios, recae en el profesional que figura como constructor del proyecto para la solicitud de la licencia de construcción. J.1.1.3	

VIVIENDA CAMPESTRE

PROYECTO:

Vereda La Cabaña, entrada a Rumichaca, Finca El Paraíso, Lote C - Manizales

PROPIETARIO

Regina Rivera Giraldo

CC 30319614

DISEÑO ARQUITECTONICO:

ARQUITECTO
FABIAN CIFUENTES
MP

ELEMENTOS NO ESTRUCTURALES:

OBSERVACIONES:

IMPRESION MONOCHROME.CTB
COLOR: BLACK
LINEWEIGHT: USE OBJECT LINEWEIGHT

Se da cumplimiento a la resolución 5004 del 2018 y a sus modificaciones con respecto a los directrices trazadas por el RITEL

MODIFICACIONES

No.	OBSERVACION	FECHA
1		
2		
3		
4		
5		

CONTIENE:

ARQUITECTONICO

FACHADA LATERAL DERECHA
FACHADA POSTERIOR
SECCION C-1
FACHADA PPAL
TITULO JYK
GRADO DESEMPEÑO

APROBO:

DIBUJO:

Digitec
Nestor Javier Sanchez Arcila
Celular: 3113333400
Email: nestorapin3@gmail.com

FECHA:

AGOSTO DE 2025

ESCALA:

1 : 50

PLANO:

2 DE: 2

ARQUITECTONICOS